


REV:01 : 01.09.2023


FASE CEILINGLAYOUT
GROUND FLOOR

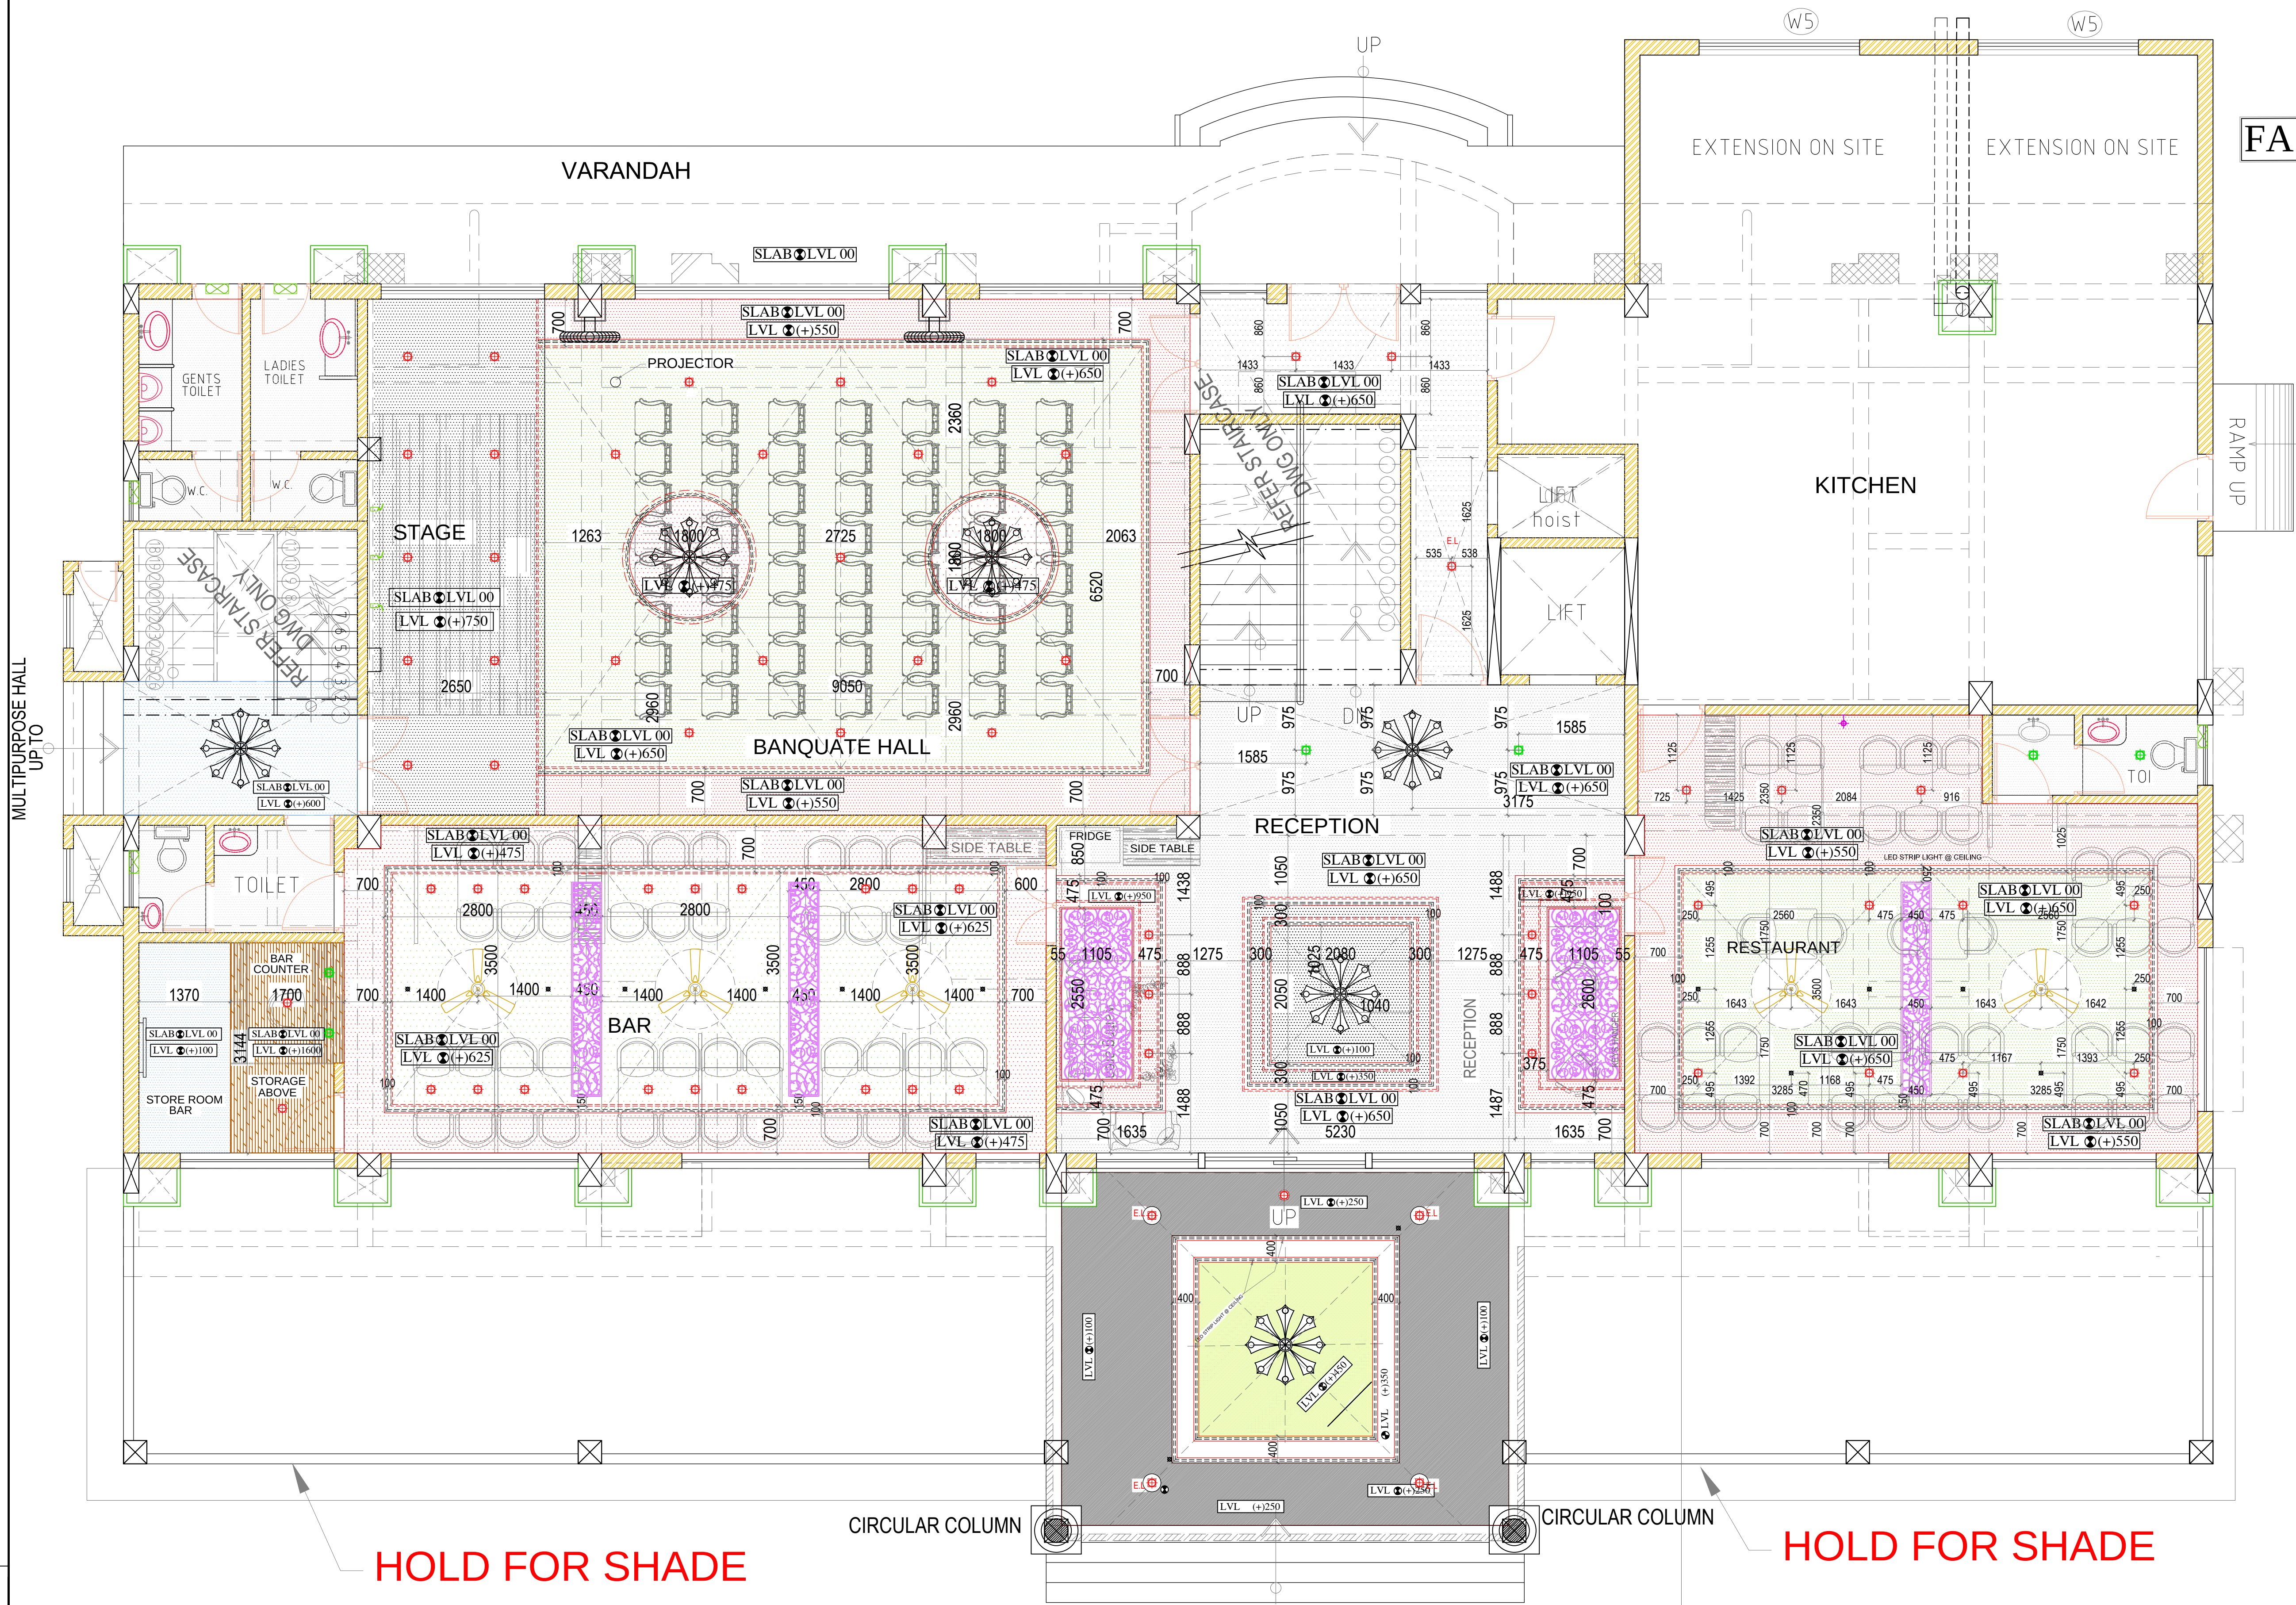

FASE CEILINGLAYOUT GROUND FLOOR

REV:01 : 01.09.2023

ELECTRICAL LAYOUT
GROUND FLOOR

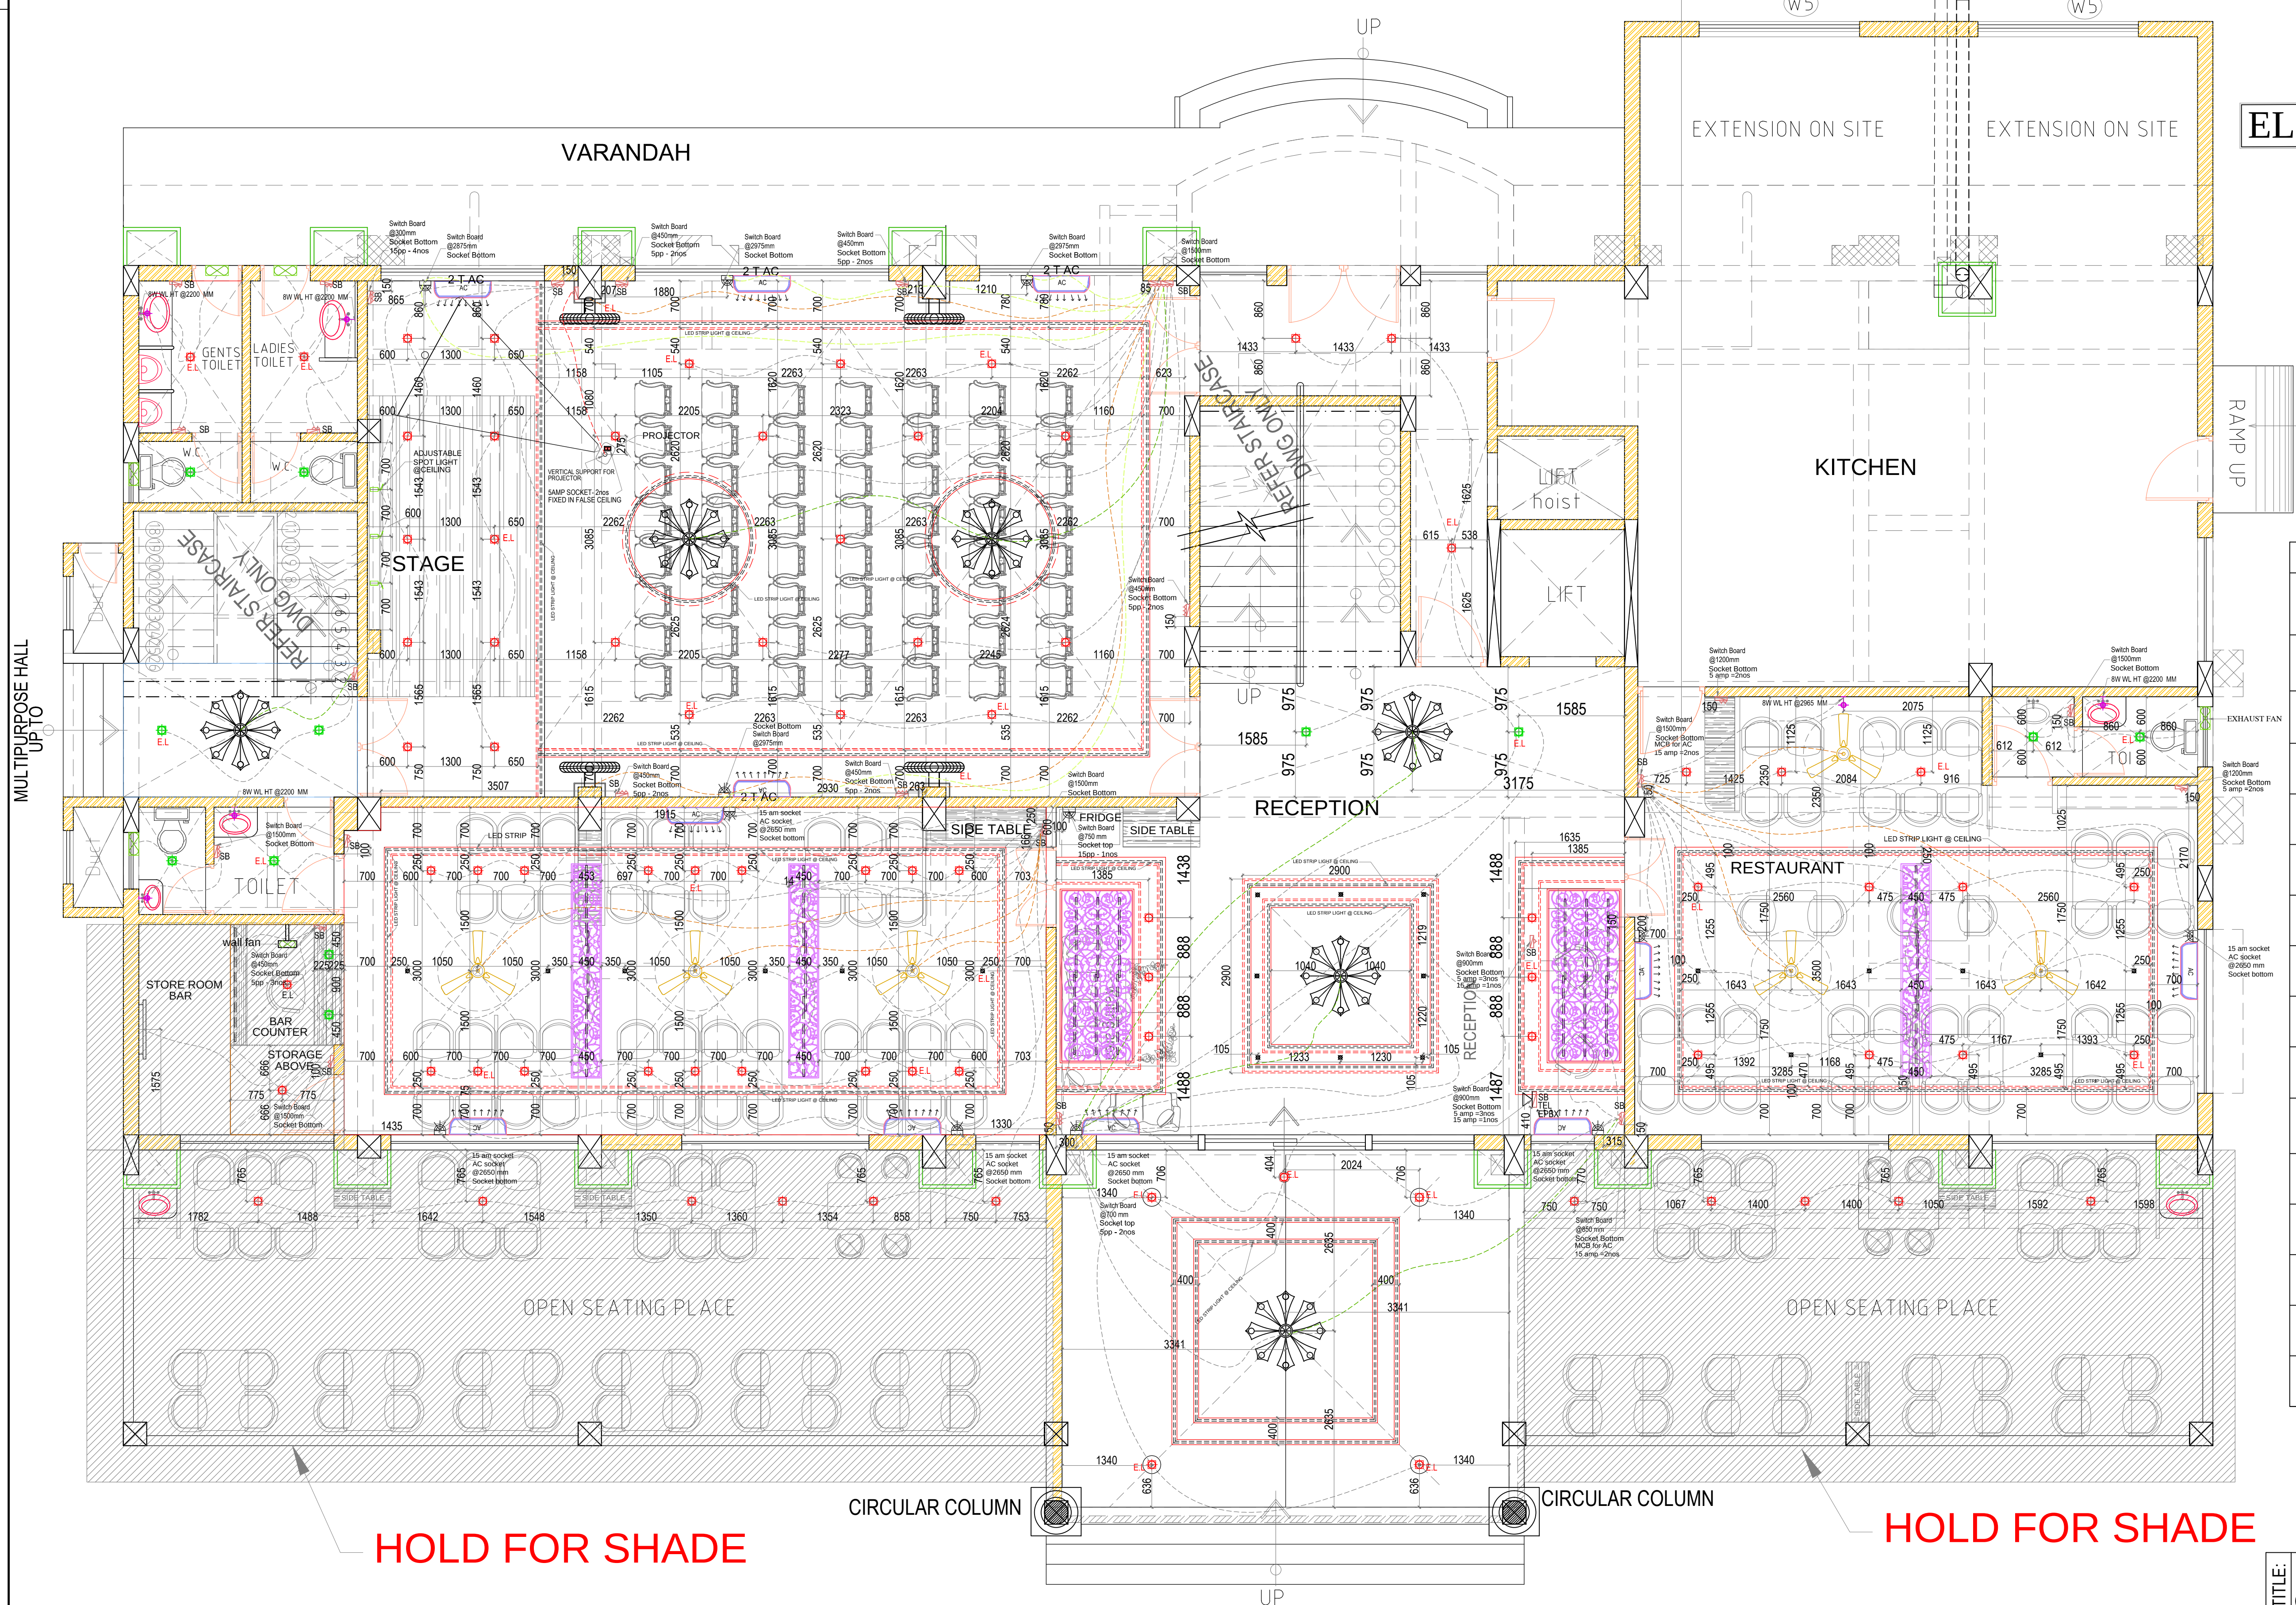

ELECTRICAL LAYOUT GROUND FLOOR

LEGENDS

[Symbol]	12W- C.O.B DELTA 1042- WHITE
[Symbol]	8W- PC PANEL WARM LIGHT
[Symbol]	6W- C.O.B DELTA 1042- WHITE
[Symbol]	EXHAUST FAN
[Symbol]	CEILING FAN
[Symbol]	SPLIT A/C
[Symbol]	15 AMP POWER POINT
[Symbol]	SWITCH BOARD
[Symbol]	TELEPHONE & INTERCOM CONNECTION
[Symbol]	WALL LIGHT POINT
[Symbol]	CHANDELIER/ZUMBER
[Symbol]	LED STRIP
[Symbol]	TUBE LIGHT
[Symbol]	WALL FAN
[Symbol]	EMERGENCE LIGHT
[Symbol]	TELEPHONE EPBX

NOTE - EL- EMERGENCE LIGHT CONNECT TO INVENTOR
**** WALL POINT MAY SHIFT AS PER INTERIOR ELEVATION****